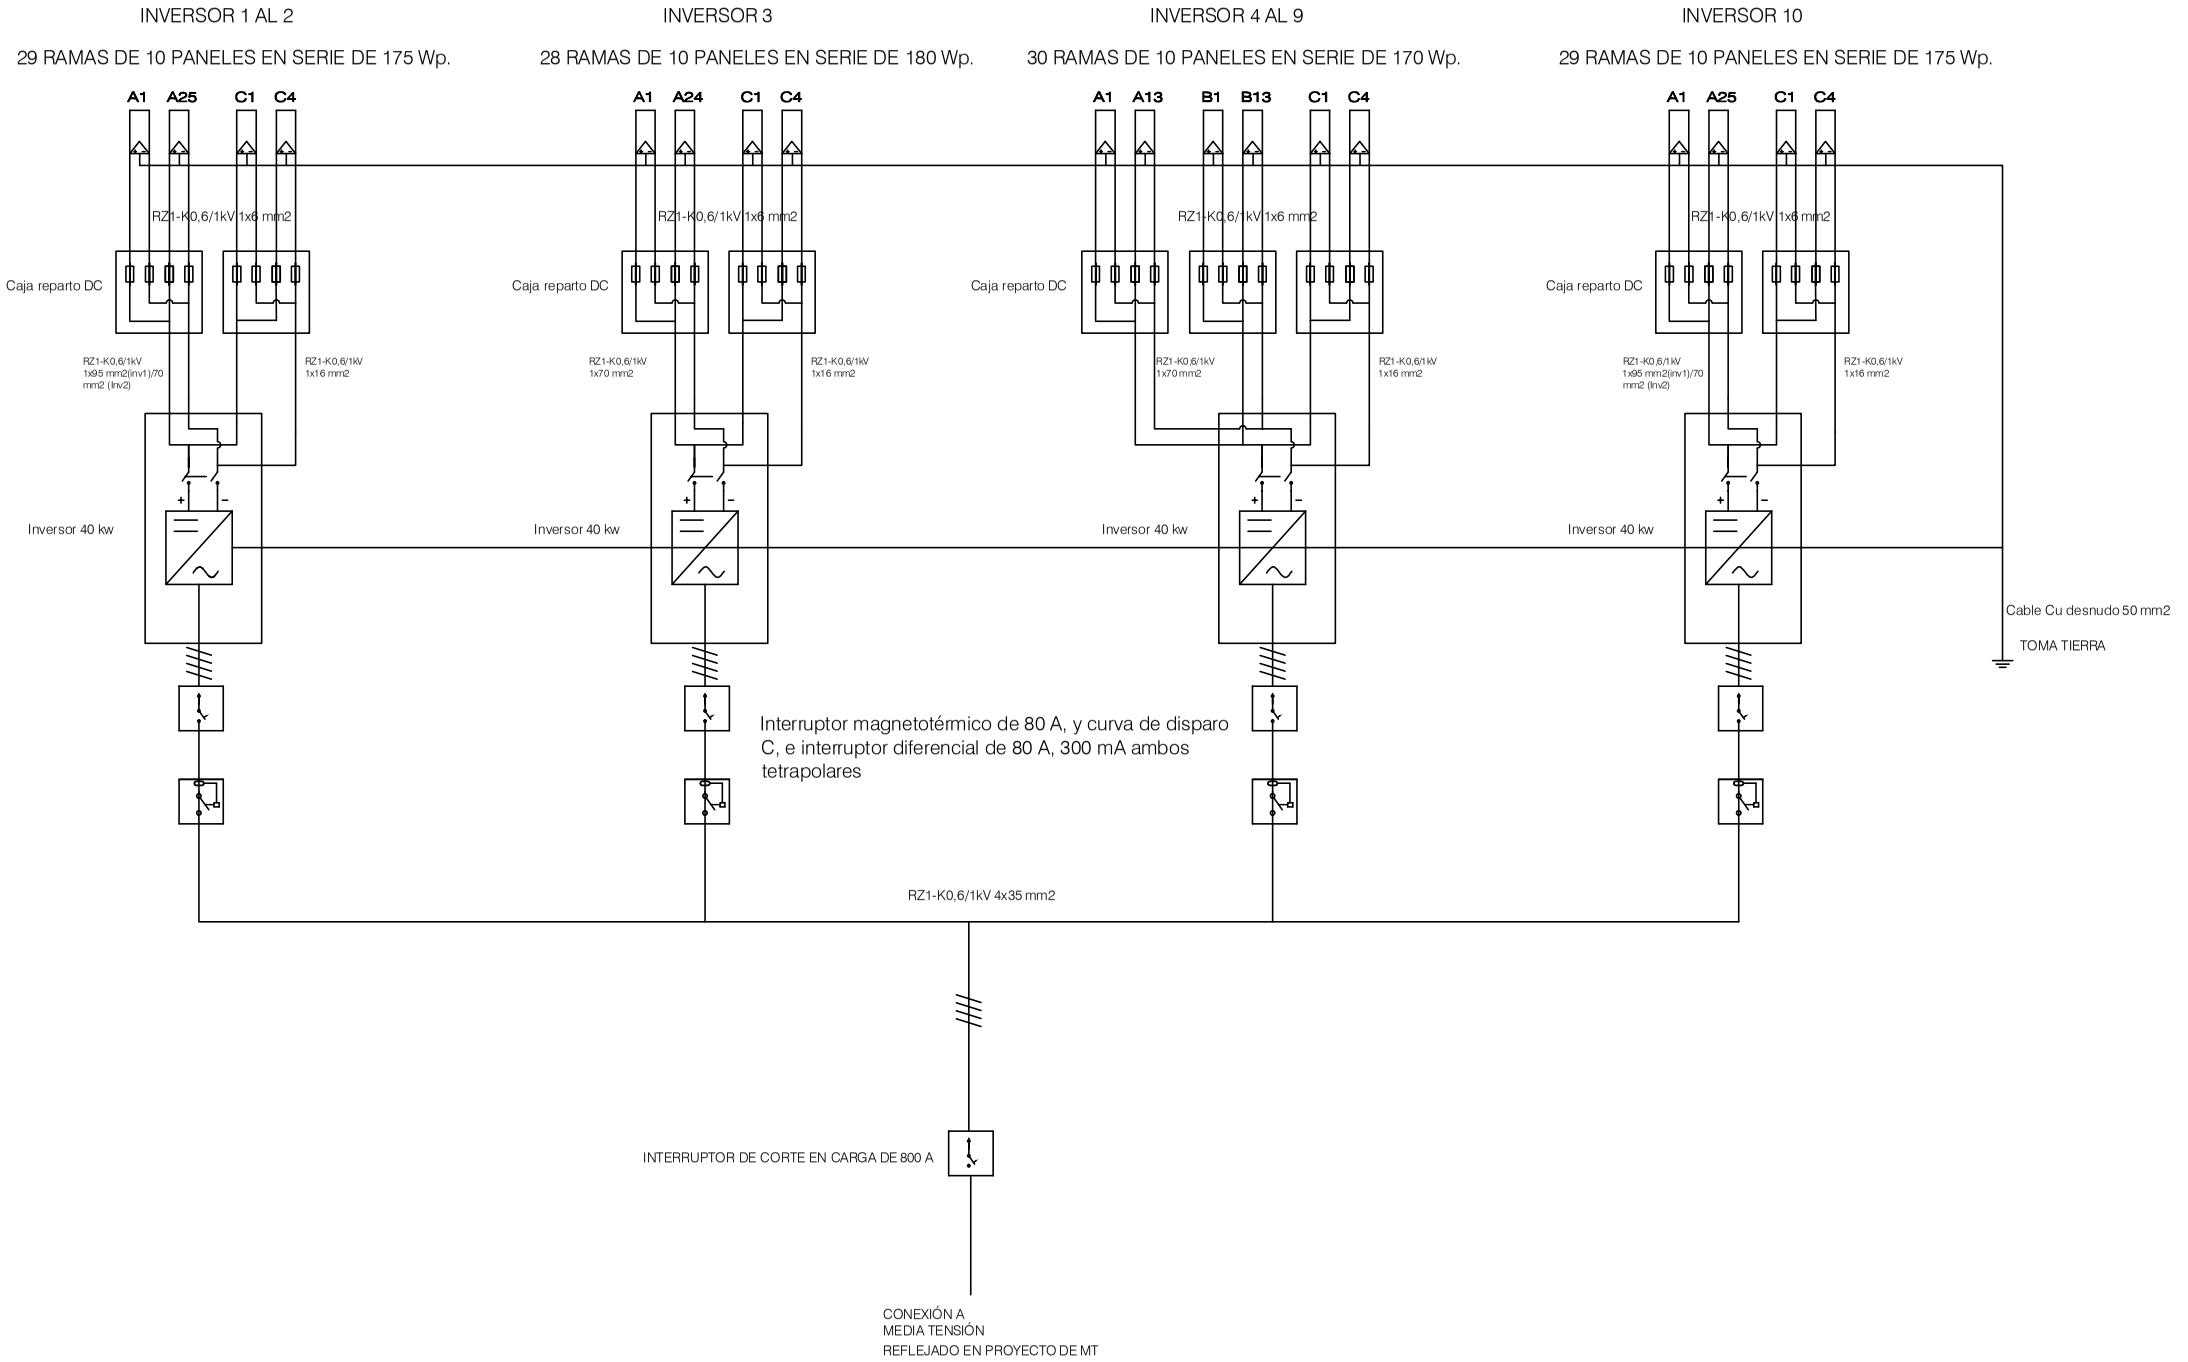
INVERSOR 1 AL 2
29 RAMAS DE 10 PANELES EN SERIE DE 175 Wp.
INVERSOR 3
28 RAMAS DE 10 PANELES EN SERIE DE 180 Wp.
INVERSOR 4 AL 9
30 RAMAS DE 10 PANELES EN SERIE DE 170 Wp.
INVERSOR 10
29 RAMAS DE 10 PANELES EN SERIE DE 175 Wp.
A1 A25 C1 C4
A1 A24 C1 C4
A1 A13 B1 B13 C1 C4
A1 A25 C1 C4
RZ1-K0,6/1kV 1x6 mm2
Caja reparto DC
RZ1-K0,6/1kV 1x95 mm2(inv1)/70 mm2 (Inv2)
RZ1-K0,6/1kV 1x16 mm2
RZ1-K0,6/1kV 1x70 mm2
Inversor 40 kw
Cable Cu desnudo 50 mm2
TOMA TIERRA
Interruptor magnetotérmico de 80 A, y curva de disparo C, e interruptor diferencial de 80 A, 300 mA ambos tetrapolares
RZ1-K0,6/1kV 4x35 mm2
INTERRUPTOR DE CORTE EN CARGA DE 800 A
CONEXIÓN A
MEDIA TENSIÓN
REFLEJADO EN PROYECTO DE MT