
GOBIERNO DE ESPAÑA
MINISTERIO DE HACIENDA
SECRETARÍA DE ESTADO DE HACIENDA
DIRECCIÓN GENERAL DEL CATASTRO
Sede Electrónica del Catastro

CROQUIS CATASTRAL


PARCELA CATASTRAL 9347902VK3994N

RD EUROPA, 0005. TRES CANTOS [Madrid]

4 de septiembre de 2026 18:49

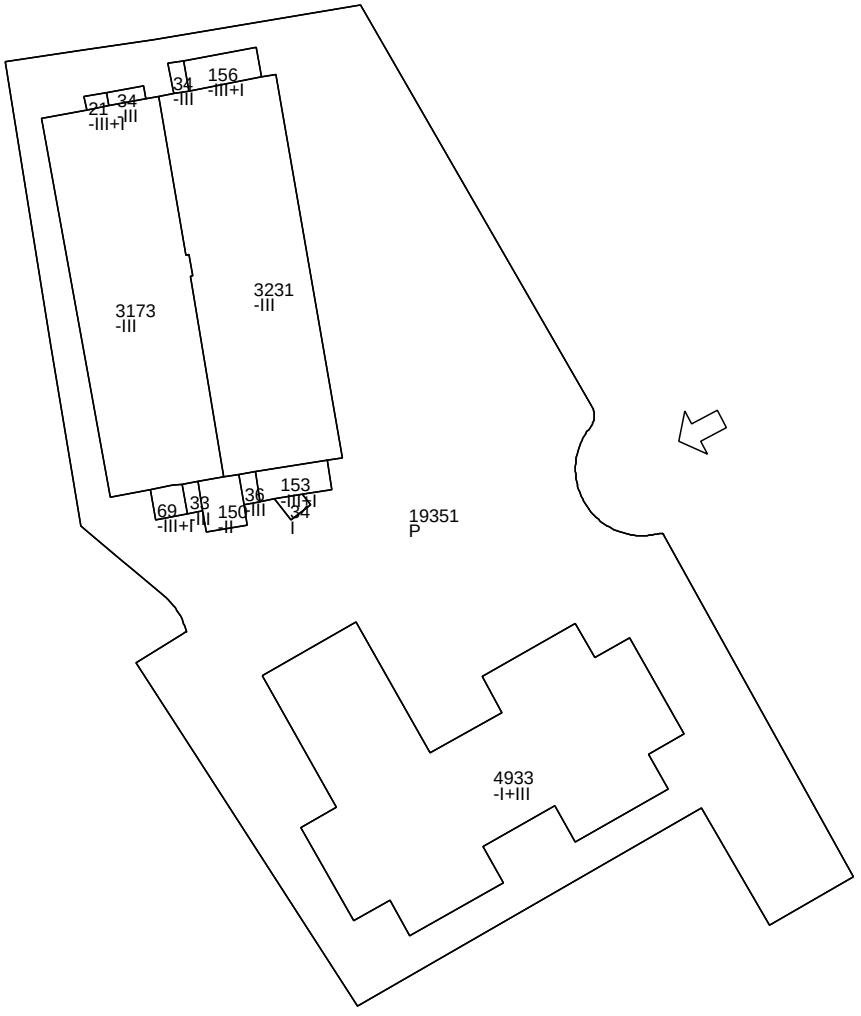

SUPERFICIE PARCELA :	31.408 m²
SUPERFICIE CONSTRUIDA	
Sobre Rasante :	15,232 m²
Bajo Rasante :	26,053 m²
TOTAL :	41,285 m²

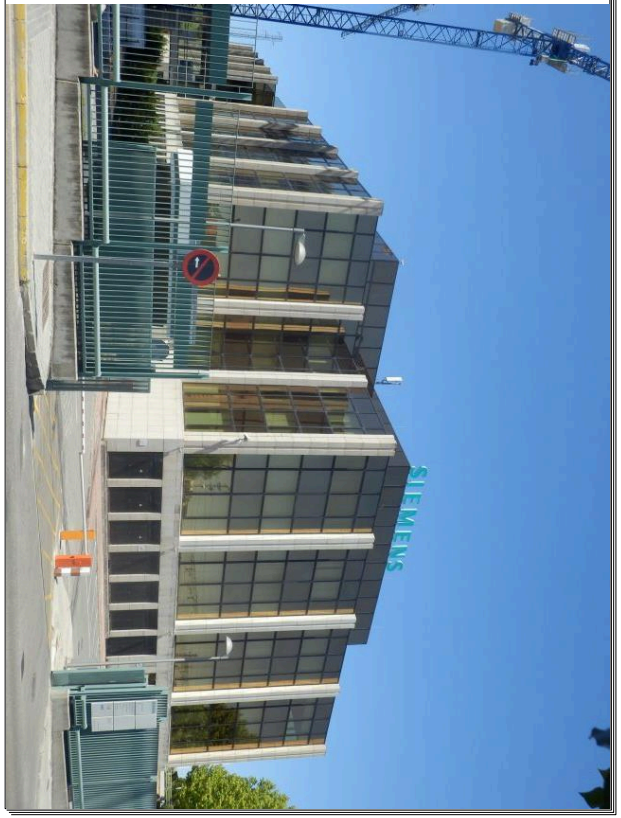

PLANTA GENERAL — CROQUIS A ESCALA 1:2000


FOTOGRAFÍA

CROQUIS CATASTRAL

PARCELA CATASTRAL 9347902VK3994N

RD EUROPA, 0005. TRES CANTOS [Madrid]

4 de septiembre de 2026 18:49

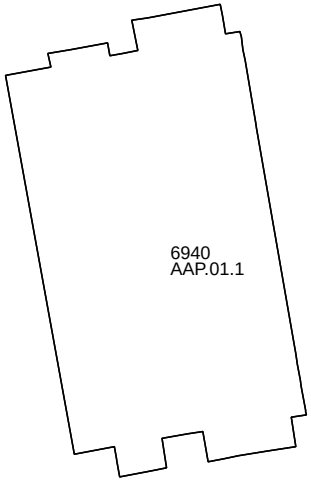

SUPERFICIE PARCELA : 31.408 m²

SUPERFICIES SEGÚN USOS

Código	Sup. en m²	Descripción
AAP.01.1	6940	APARCAMIENTO
TOTAL	**6940**	

SUPERFICIES GRÁFICAS

Código	Sup. en m²	Descripción
AAP.01.1	6940	APARCAMIENTO
TOTAL	**6940**	

PLANTA SOTANO -3


CROQUIS A ESCALA 1:2000

CROQUIS CATASTRAL

PARCELA CATASTRAL 9347902VK3994N

RD EUROPA, 0005. TRES CANTOS [Madrid]

4 de septiembre de 2026 18:49

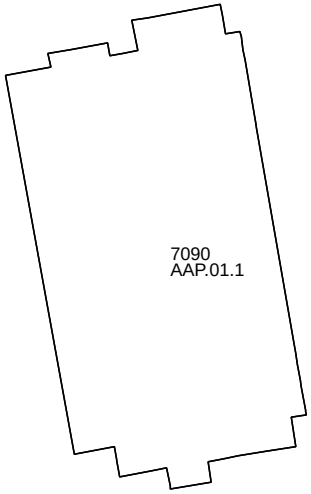

SUPERFICIE PARCELA : 31.408 m²

SUPERFICIES SEGÚN USOS

Código	Sup. en m²	Descripción
AAP.01.1	7090	APARCAMIENTO
TOTAL	**7090**	

SUPERFICIES GRÁFICAS

Código	Sup. en m²	Descripción
AAP.01.1	7090	APARCAMIENTO
TOTAL	**7090**	

PLANTA SOTANO -2


CROQUIS A ESCALA 1:2000

CROQUIS CATASTRAL

PARCELA CATASTRAL 9347902VK3994N

RD EUROPA, 0005. TRES CANTOS [Madrid]

4 de septiembre de 2026 18:49

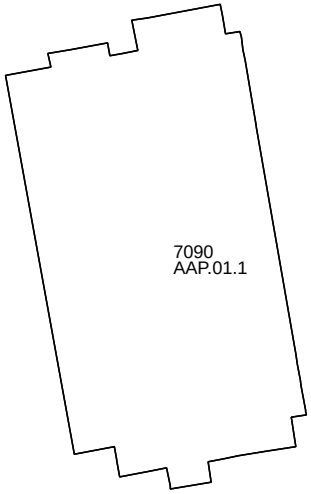

SUPERFICIE PARCELA : 31.408 m²

SUPERFICIES SEGÚN USOS

Código	Sup. en m²	Descripción
AAP.01.1	7090	APARCAMIENTO
TOTAL	**7090**	

SUPERFICIES GRÁFICAS

Código	Sup. en m²	Descripción
AAP.01.1	7090	APARCAMIENTO
TOTAL	**7090**	

PLANTA SOTANO -1


CROQUIS A ESCALA 1:2000

CROQUIS CATASTRAL

PARCELA CATASTRAL 9347902VK3994N

RD EUROPA, 0005. TRES CANTOS [Madrid]

4 de septiembre de 2026 18:49

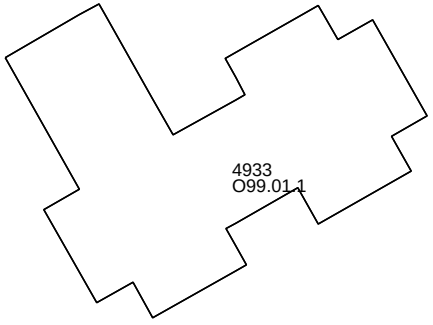

SUPERFICIE PARCELA : 31.408 m²

SUPERFICIES SEGÚN USOS

Código	Sup. en m²	Descripción
O99.01.1	4933	O99
TOTAL	**4933**	

SUPERFICIES GRÁFICAS


Código	Sup. en m²	Descripción
O99.01.1	4933	O99
TOTAL	**4933**	

CROQUIS CATASTRAL

PARCELA CATASTRAL 9347902VK3994N

RD EUROPA, 0005. TRES CANTOS [Madrid]

4 de septiembre de 2026 18:49

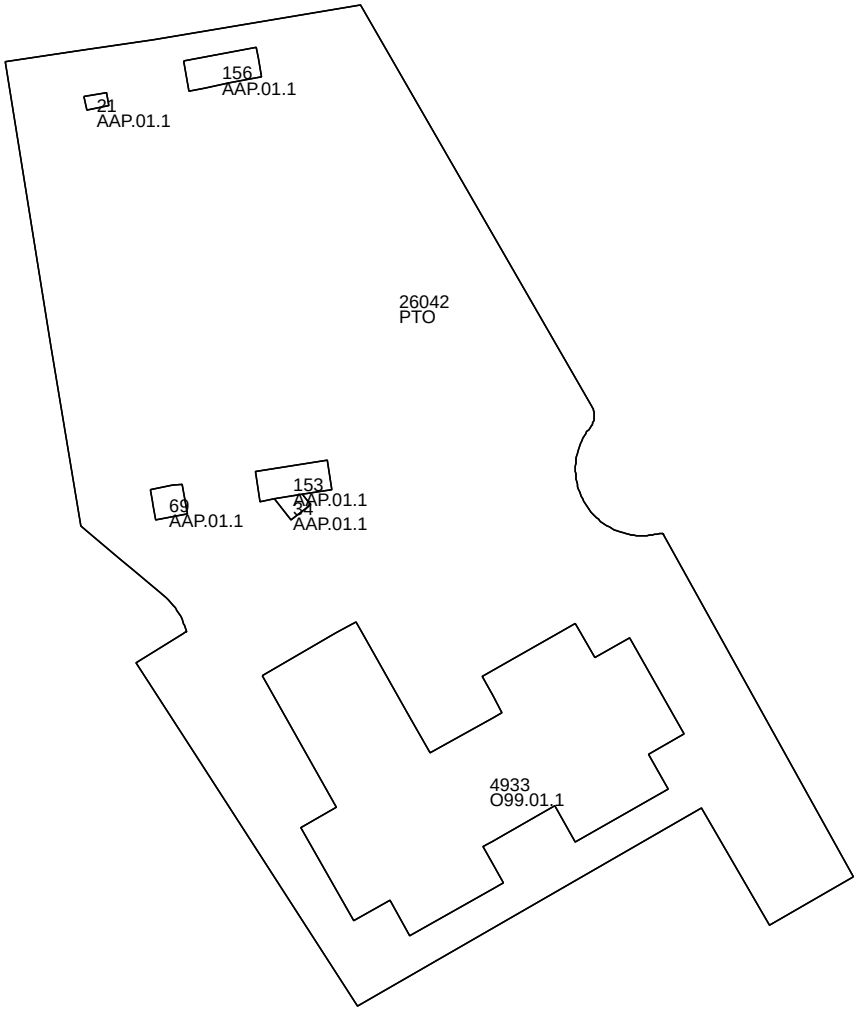

SUPERFICIE PARCELA : 31.408 m²

SUPERFICIES SEGÚN USOS

Código	Sup. en m²	Descripción
AAP.01.1	433	APARCAMIENTO
O99.01.1	4933	O99
TOTAL	**5366**	

SUPERFICIES GRÁFICAS

Código	Sup. en m²	Descripción
AAP.01.1	433	APARCAMIENTO
O99.01.1	4933	O99
PTO	26042	PATIO
TOTAL	**31408**	


GOBIERNO DE ESPAÑA
MINISTERIO DE HACIENDA
SECRETARÍA DE ESTADO DE HACIENDA
DIRECCIÓN GENERAL DEL CATASTRO
Sede Electrónica del Catastro

CROQUIS CATASTRAL

PARCELA CATASTRAL 9347902VK3994N

RD EUROPA, 0005. TRES CANTOS [Madrid]

4 de septiembre de 2026 18:49

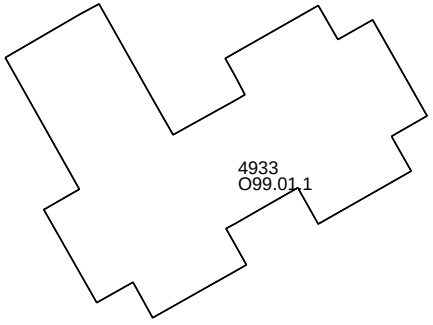

SUPERFICIE PARCELA : 31.408 m²

SUPERFICIES SEGÚN USOS

Código	Sup. en m²	Descripción
O99.01.1	4933	O99
TOTAL	**4933**	

SUPERFICIES GRÁFICAS


Código	Sup. en m²	Descripción
O99.01.1	4933	O99
TOTAL	**4933**	

CROQUIS CATASTRAL

PARCELA CATASTRAL 9347902VK3994N

RD EUROPA, 0005. TRES CANTOS [Madrid]

4 de septiembre de 2026 18:49

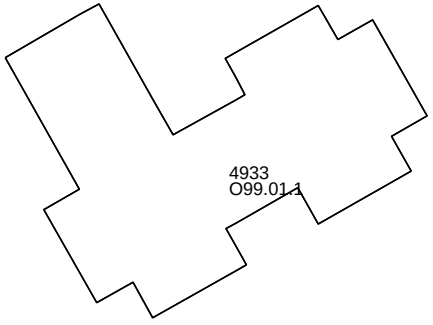

SUPERFICIE PARCELA : 31.408 m²

SUPERFICIES SEGÚN USOS

Código	Sup. en m²	Descripción
O99.01.1	4933	O99
TOTAL	**4933**	

SUPERFICIES GRÁFICAS

Código	Sup. en m²	Descripción
O99.01.1	4933	O99
TOTAL	**4933**	