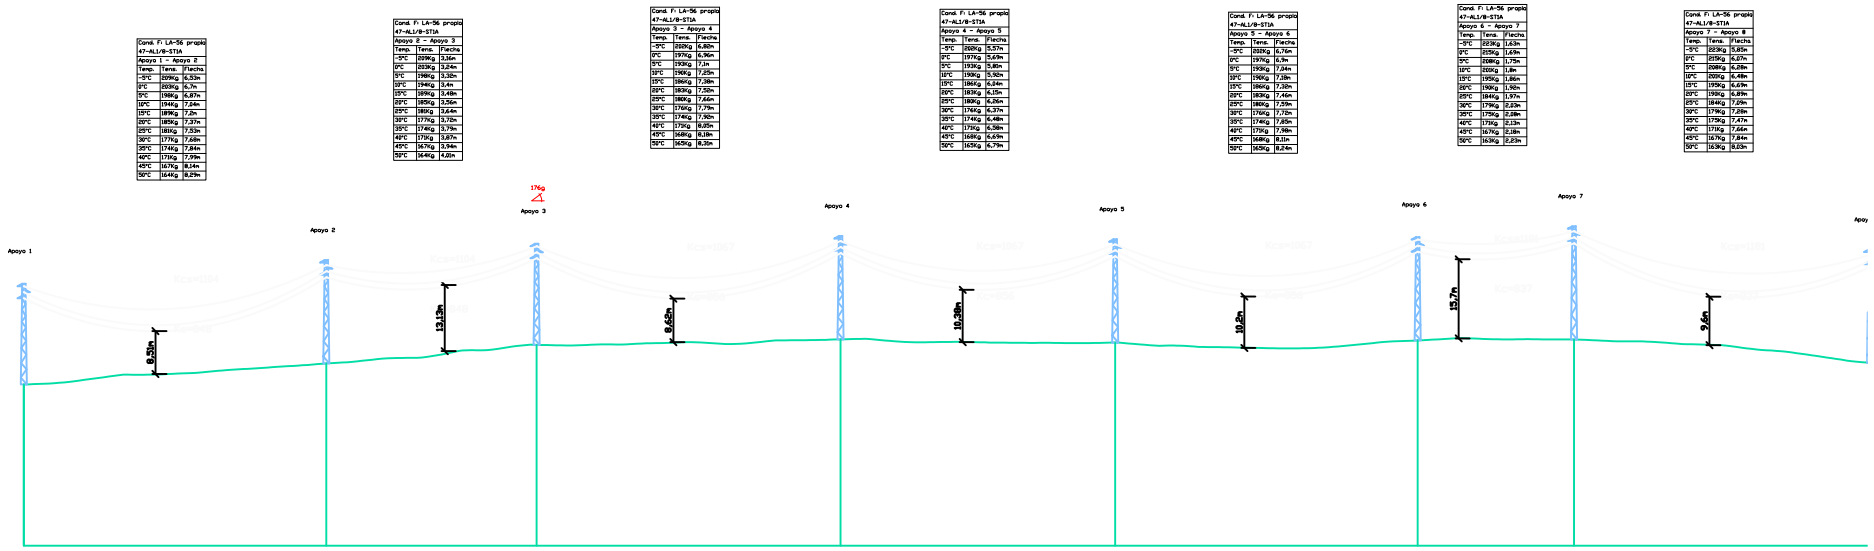

P.C.: -36.70 m													
Nº Apoyos / Longitud Vanos (m)	1	240.00	2	166.95	3	241.05	4	218.00	5	240.00	6	124.00	7	235.00
Cota Terreno (m)	-4.70		-0.55		3.14		4.23		3.60		4.02		4.19	
Distancia Parcial (m)	0.00		240.00		166.95		241.05		218.00		240.00		124.00	
Distancia Origen (m)	0.00		240.00		406.95		648.00		866.00		1106.00		1230.00	
Función de Apoyo	FL		AL_SU		AN_AM (176g)		AL_SU		AL_SU		AL_AM		AL_SU	
Serie Apoyo	C-2000-22		C-500-22		C-1000-22		C-500-22		C-500-22		C-500-22		C-500-24	
Armado (m)	b=1,2/a=1,25/c=1,25		b=1,2/a=1,25/c=1,25		b=1,2/a=1,25/c=1,25		b=1,2/a=1,25/c=1,25		b=1,2/a=1,25/c=1,25		b=1,2/a=1,25/c=1,25		b=1,2/a=1,25/c=1,25	
Altura Útil Cruceta Inferior (m)	17,07 (Normal/K=12)		17,6 (Normal/K=12)		17,16 (Normal/K=12)		17,6 (Normal/K=12)		17,6 (Normal/K=12)		17,6 (Normal/K=12)		19,58 (Normal/K=12)	
Tipo de cimentación	Monobloque		Monobloque		Monobloque		Monobloque		Monobloque		Monobloque		Monobloque	
Datos Cimentación (m)	a=1,38/h=2,13		a=1,31/h=1,6		a=1,31/h=1,84		a=1,31/h=1,6		a=1,31/h=1,6		a=1,31/h=1,6		a=1,39/h=1,62	

	Nombre	Firmas	Tipo de documento	Tolerancias generales
Creado por	Mario Carrión Sirvent		PERFIL LONGITUDINAL	
Aprobado por				

escuela técnica superior de ingeniería diseño industrial

Fecha de edición 22-12-2025

ESCALA 1:6000

U.DIM.

DETALLE APOYOS 1-7

HOJA Nº 1/1

E.T.S. DE INGENIERÍA Y DISEÑO INDUSTRIAL

Nº 00.00.00