Cond. F: LA-56 propio 47-AL1/8-ST1A		
Apoyo 5 - Apoyo 6		
Temp.	Tens.	Flecha
-5°C	202Kg	6,76m
0°C	197Kg	6,9m
5°C	193Kg	7,04m
10°C	190Kg	7,18m
15°C	186Kg	7,32m
20°C	183Kg	7,46m
25°C	180Kg	7,59m
30°C	176Kg	7,72m
35°C	174Kg	7,85m
40°C	171Kg	7,98m
45°C	168Kg	8,11m
50°C	165Kg	8,24m

Cond. F: LA-56 propio 47-AL1/8-ST1A		
Apoyo 6 - Apoyo 7		
Temp.	Tens.	Flecha
-5°C	223Kg	1,63m
0°C	215Kg	1,69m
5°C	208Kg	1,75m
10°C	201Kg	1,8m
15°C	195Kg	1,86m
20°C	190Kg	1,92m
25°C	184Kg	1,97m
30°C	179Kg	2,03m
35°C	175Kg	2,08m
40°C	171Kg	2,13m
45°C	167Kg	2,18m
50°C	163Kg	2,23m

Cond. F: LA-56 propio 47-AL1/8-ST1A		
Apoyo 7 - Apoyo 8		
Temp.	Tens.	Flecha
-5°C	223Kg	5,85m
0°C	215Kg	6,07m
5°C	208Kg	6,28m
10°C	201Kg	6,48m
15°C	195Kg	6,69m
20°C	190Kg	6,89m
25°C	184Kg	7,09m
30°C	179Kg	7,28m
35°C	175Kg	7,47m
40°C	171Kg	7,66m
45°C	167Kg	7,84m
50°C	163Kg	8,03m

Cond. F: LA-56 propio 47-AL1/8-ST1A		
Apoyo 8 - Apoyo 9		
Temp.	Tens.	Flecha
-5°C	223Kg	1,63m
0°C	215Kg	1,69m
5°C	208Kg	1,75m
10°C	201Kg	1,81m
15°C	195Kg	1,87m
20°C	190Kg	1,92m
25°C	184Kg	1,98m
30°C	179Kg	2,03m
35°C	175Kg	2,09m
40°C	171Kg	2,14m
45°C	167Kg	2,19m
50°C	163Kg	2,24m

Cond. F: LA-56 propio 47-AL1/8-ST1A		
Apoyo 9 - Apoyo 10		
Temp.	Tens.	Flecha
-5°C	219Kg	1,74m
0°C	212Kg	1,8m
5°C	205Kg	1,86m
10°C	199Kg	1,92m
15°C	193Kg	1,97m
20°C	188Kg	2,03m
25°C	183Kg	2,08m
30°C	179Kg	2,13m
35°C	174Kg	2,19m
40°C	170Kg	2,24m
45°C	167Kg	2,29m
50°C	163Kg	2,34m

Cond. F: LA-56 propio 47-AL1/8-ST1A		
Apoyo 10 - Apoyo 11		
Temp.	Tens.	Flecha
-5°C	219Kg	2,98m
0°C	212Kg	3,08m
5°C	205Kg	3,18m
10°C	199Kg	3,27m
15°C	193Kg	3,37m
20°C	188Kg	3,46m
25°C	183Kg	3,56m
30°C	179Kg	3,65m
35°C	174Kg	3,74m
40°C	170Kg	3,82m
45°C	167Kg	3,91m
50°C	163Kg	4m

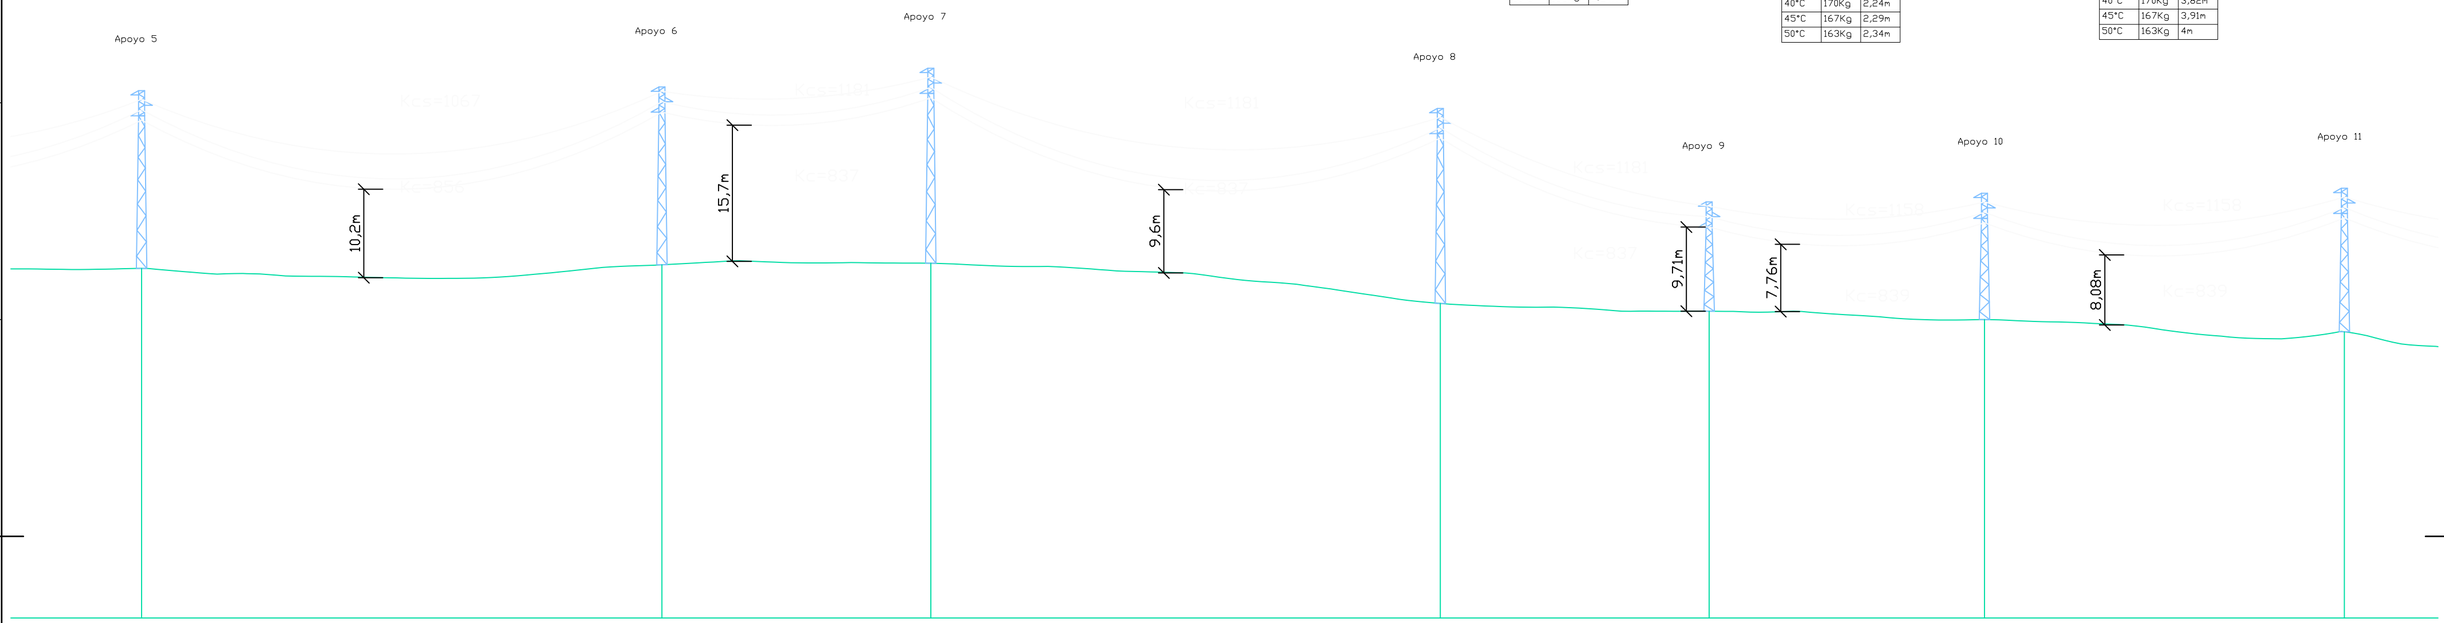

5	240.00	6	124.00	7	235.00	8	124.00	9	127.00	10	166.00	11
3.60		4.02		4.19		-0.44		-1.34		-2.30		-3.71
218.00		240.00		124.00		235.00		124.00		127.00		166.00
866.00		1106.00		1230.00		1465.00		1589.00		1716.00		1882.00
AL_SU		AL_AM		AL_SU		AL_SU		AL_AM		AL_SU		AL_SU
C-500-22		C-500-22		C-500-24		C-500-24		C-500-14		C-500-16		C-500-18
b=1,2/a=1,25/c=1,25		b=1,2/a=1,25/c=1,25		b=1,2/a=1,25/c=1,25		b=1,2/a=1,25/c=1,25		b=1,2/a=1,25/c=1,25		b=1,2/a=1,25/c=1,25		b=1,2/a=1,2
17,6 (Normal/K=12)		17,6 (Normal/K=12)		19,58 (Normal/K=12)		19,58 (Normal/K=12)		9,71 (Normal/K=12)		11,67 (Normal/K=12)		13,65 (Nor
Monobloque		Monobloque		Monobloque		Monobloque		Monobloque		Monobloque		Monobloque
a=1,31/h=1,6		a=1,31/h=1,6		a=1,39/h=1,62		a=1,39/h=1,62		a=1,01/h=1,49		a=1,08/h=1,53		a=1,16/h=1,

	Nombre	Firmas	Tipo de documento	Tolerancias generales
Creado por	Mario Carrión Sirvent		PERFIL LONGITUDINAL	
Aprobado por				

escuela técnica superior de ingeniería y diseño industrial

ESCALA 1:2000

U.DIM.

DETALLE APOYOS 5-11

HOJA Nº 1/1

22/12/2025

E.T.S. DE INGENIERÍA Y DISEÑO INDUSTRIAL

Nº 1