
Cond. Fi LA-56 propio 47-AL1/8-ST1A		
Apoyo 1 - Apoyo 2		
Temp.	Tens.	Flecha
-5°C	209Kg	6,53m
0°C	203Kg	6,7m
5°C	198Kg	6,87m
10°C	194Kg	7,04m
15°C	189Kg	7,2m
20°C	185Kg	7,37m
25°C	181Kg	7,53m
30°C	177Kg	7,68m
35°C	174Kg	7,84m
40°C	171Kg	7,99m
45°C	167Kg	8,14m
50°C	164Kg	8,29m

Cond. Fi LA-56 propio 47-AL1/8-ST1A		
Apoyo 2 - Apoyo 3		
Temp.	Tens.	Flecha
-5°C	209Kg	3,16m
0°C	203Kg	3,24m
5°C	198Kg	3,32m
10°C	194Kg	3,4m
15°C	189Kg	3,48m
20°C	185Kg	3,56m
25°C	181Kg	3,64m
30°C	177Kg	3,72m
35°C	174Kg	3,79m
40°C	171Kg	3,87m
45°C	167Kg	3,94m
50°C	164Kg	4,01m

Cond. Fi LA-56 propio 47-AL1/8-ST1A		
Apoyo 3 - Apoyo 4		
Temp.	Tens.	Flecha
-5°C	202Kg	6,82m
0°C	197Kg	6,96m
5°C	193Kg	7,1m
10°C	190Kg	7,25m
15°C	186Kg	7,38m
20°C	183Kg	7,52m
25°C	180Kg	7,66m
30°C	176Kg	7,79m
35°C	174Kg	7,92m
40°C	171Kg	8,05m
45°C	168Kg	8,18m
50°C	165Kg	8,31m

Cond. Fi LA-56 propio 47-AL1/8-ST1A		
Apoyo 4 - Apoyo 5		
Temp.	Tens.	Flecha
-5°C	202Kg	5,57m
0°C	197Kg	5,69m
5°C	193Kg	5,81m
10°C	190Kg	5,92m
15°C	186Kg	6,04m
20°C	183Kg	6,15m
25°C	180Kg	6,26m
30°C	176Kg	6,37m
35°C	174Kg	6,48m
40°C	171Kg	6,58m
45°C	168Kg	6,69m
50°C	165Kg	6,79m

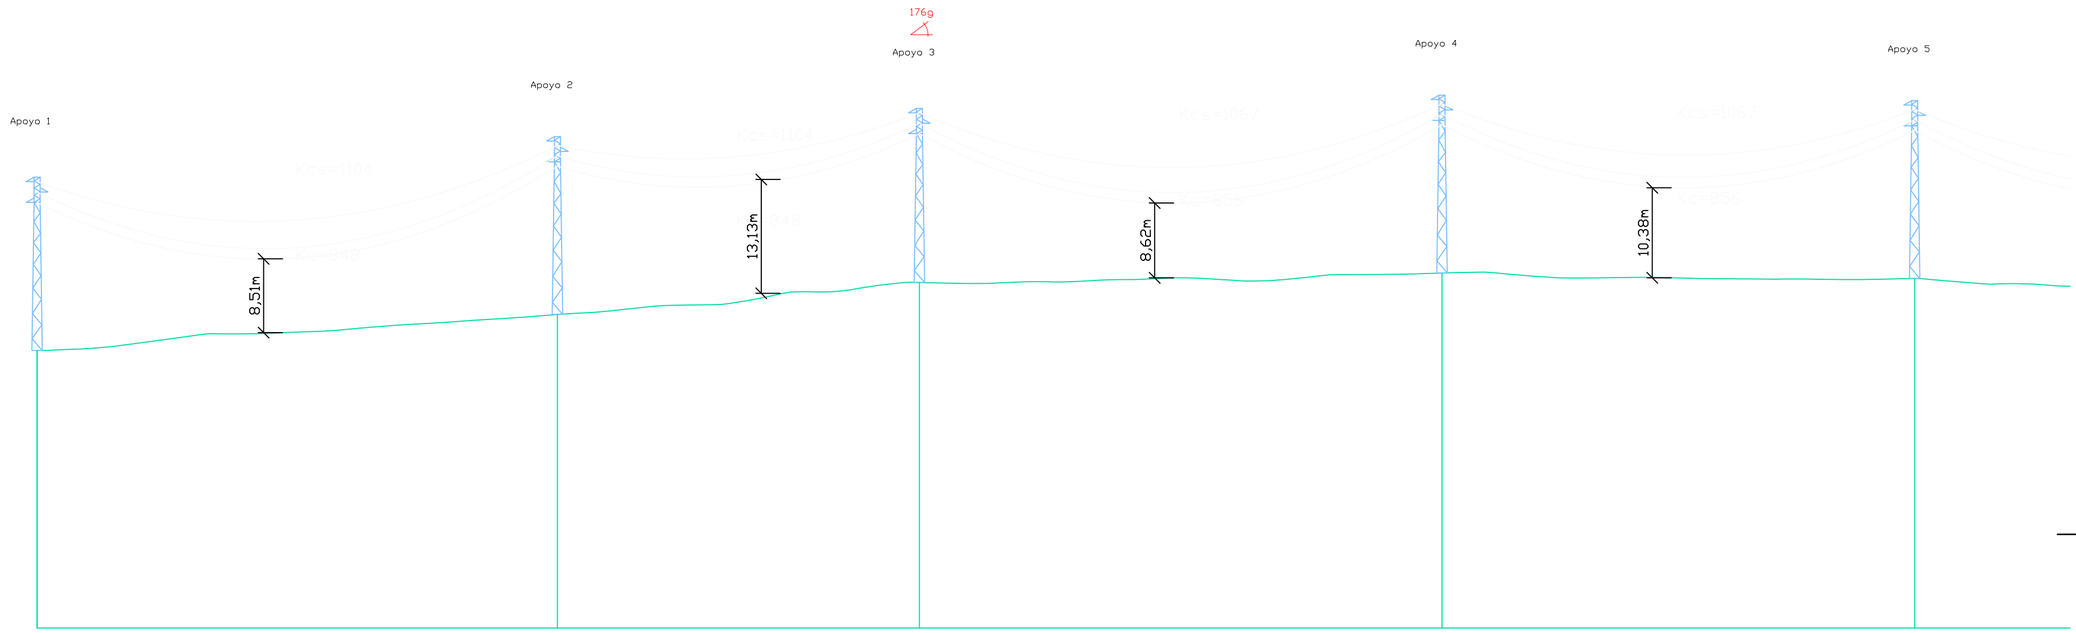

P.C.: -36.70 m

Nº Apoyos / Longitud Vanos (m)	1	240.00	2	166.95	3	241.05	4	218.00	5
Cota Terreno (m)	-4.70		-0.55		3.14		4.23		3.60
Distancia Parcial (m)	0.00		240.00		166.95		241.05		218.00
Distancia Origen (m)	0.00		240.00		406.95		648.00		866.00
Función de Apoyo	FL		AL_SU		AN_AM (176g)		AL_SU		AL_SU
Serie Apoyo	C-2000-22		C-500-22		C-1000-22		C-500-22		C-500-22
Armado (m)	b=1,2/a=1,25/c=1,25		b=1,2/a=1,25/c=1,25		b=1,2/a=1,25/c=1,25		b=1,2/a=1,25/c=1,25		b=1,2/a=1,25/c=1,
Altura Util Cruceta Inferior (m)	17,07 (Normal/K=12)		17,6 (Normal/K=12)		17,16 (Normal/K=12)		17,6 (Normal/K=12)		17,6 (Normal/K=12
Tipo de cimentación	Monobloque		Monobloque		Monobloque		Monobloque		Monobloque
Datos Cimentación (m)	a=1,38/h=2,13		a=1,31/h=1,6		a=1,31/h=1,84		a=1,31/h=1,6		a=1,31/h=1,6

	Nombre	Firmas	Tipo de documento	Tolerancias generales
Creado por	Mario Carrión Sirvent		PERFIL LONGITUDINAL	
Aprobado por				
escuela técnica superior de ingeniería diseño industrial	ESCALA 1:2000	DETALLE APOYOS 1-5		HOJA Nº 1/1
22/12/2025	U.DIM.	E.T.S. DE INGENIERÍA Y DISEÑO INDUSTRIAL		Nº 1